
PROGRESS DRAWINGS

FA
X: 844880773
Y: 831779436

FB
X: 844880796
Y: 831788298

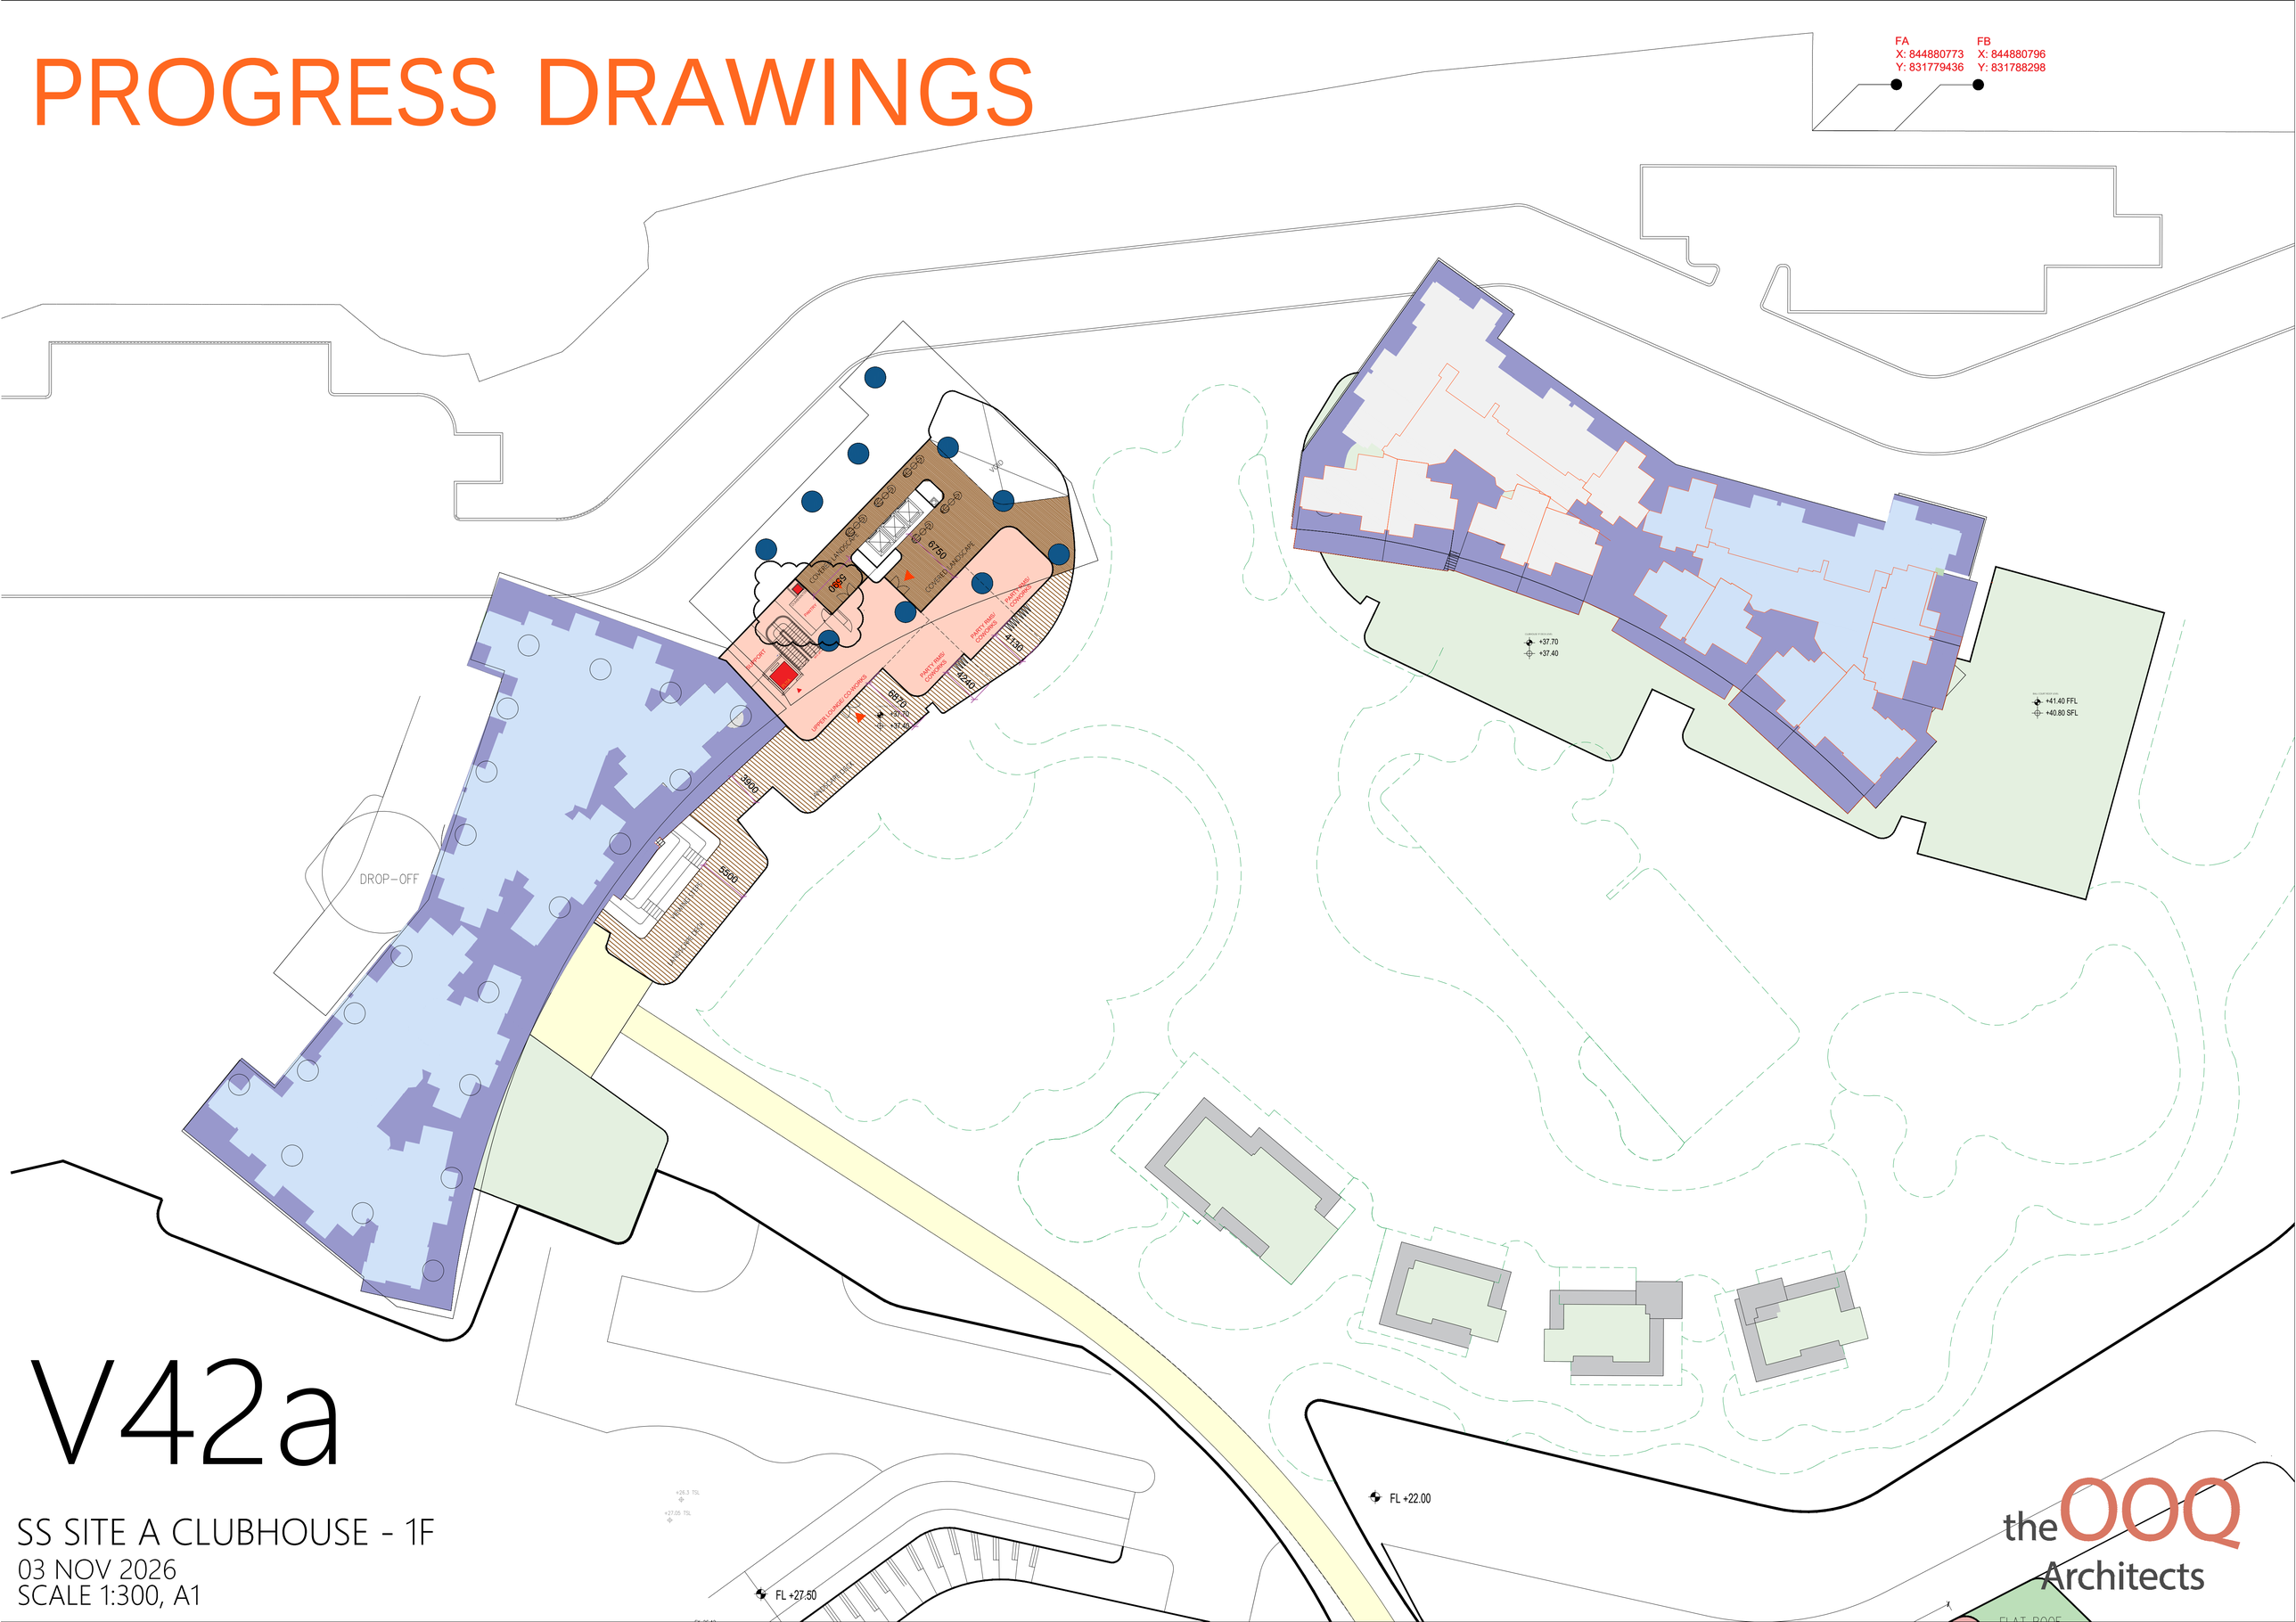

V42a

SS SITE A CLUBHOUSE - 1F

03 NOV 2026

SCALE 1:300, A1

the OOQ Architects

PROGRESS DRAWINGS

FA
X: 844880773
Y: 831779436

FB
X: 844880796
Y: 831788298

ENTRANCE FOYER
SUPPORT
BAR
KITCHEN
BATTLE UP
ACTIVITY RM
+32.70
+32.60
DROP–OFF
1200Ø
GYM
(275 SQM)
MAIN SHUTTLE LIFT
LANDSCAPE DECK FOR OUTDOOR GYM
CHILDREN PLAY
(260 SQM)
FEATURE POOL
GRAND LAWN
MAIN GYM 2
(110 sqm)
INDOOR POOL
+32.60 WL
+31.40 FPL
+31.20 SPL
GAME ZONE
MAIN GYM
CARPARK ENTRY
BALL COURT
(650 sqm)
FL +22.00
FL +27.50

V42a

SS SITE A CLUBHOUSE
03 NOV 2026
SCALE 1:300, A1

the OOQ Architects