


- BUILDING ABOVE/
COVERED LANDSCAPE/
CANOPY
- CLUBHOUSE/ TOWER LOBBY
- 1350mm SOIL
- 750mm SOIL
- 450mm SOIL
- 300mm POOL
- 1200mm POOL
- METAL COVERED WALKWAY
(3500mm W)
- PREVIOUS DIRECTOR HSES

UG2 MAIN CLUBHOUSE LEVEL
+32.70
+32.60

LANDSCAPE TOP OF SOIL LEVEL
+32.70 TOS

SWIMMING POOL LEVEL
+32.60 WL
+31.40 FFL
+31.20 SFL

FA X: 844880773 Y: 831779436
FB X: 844880796 Y: 831788298

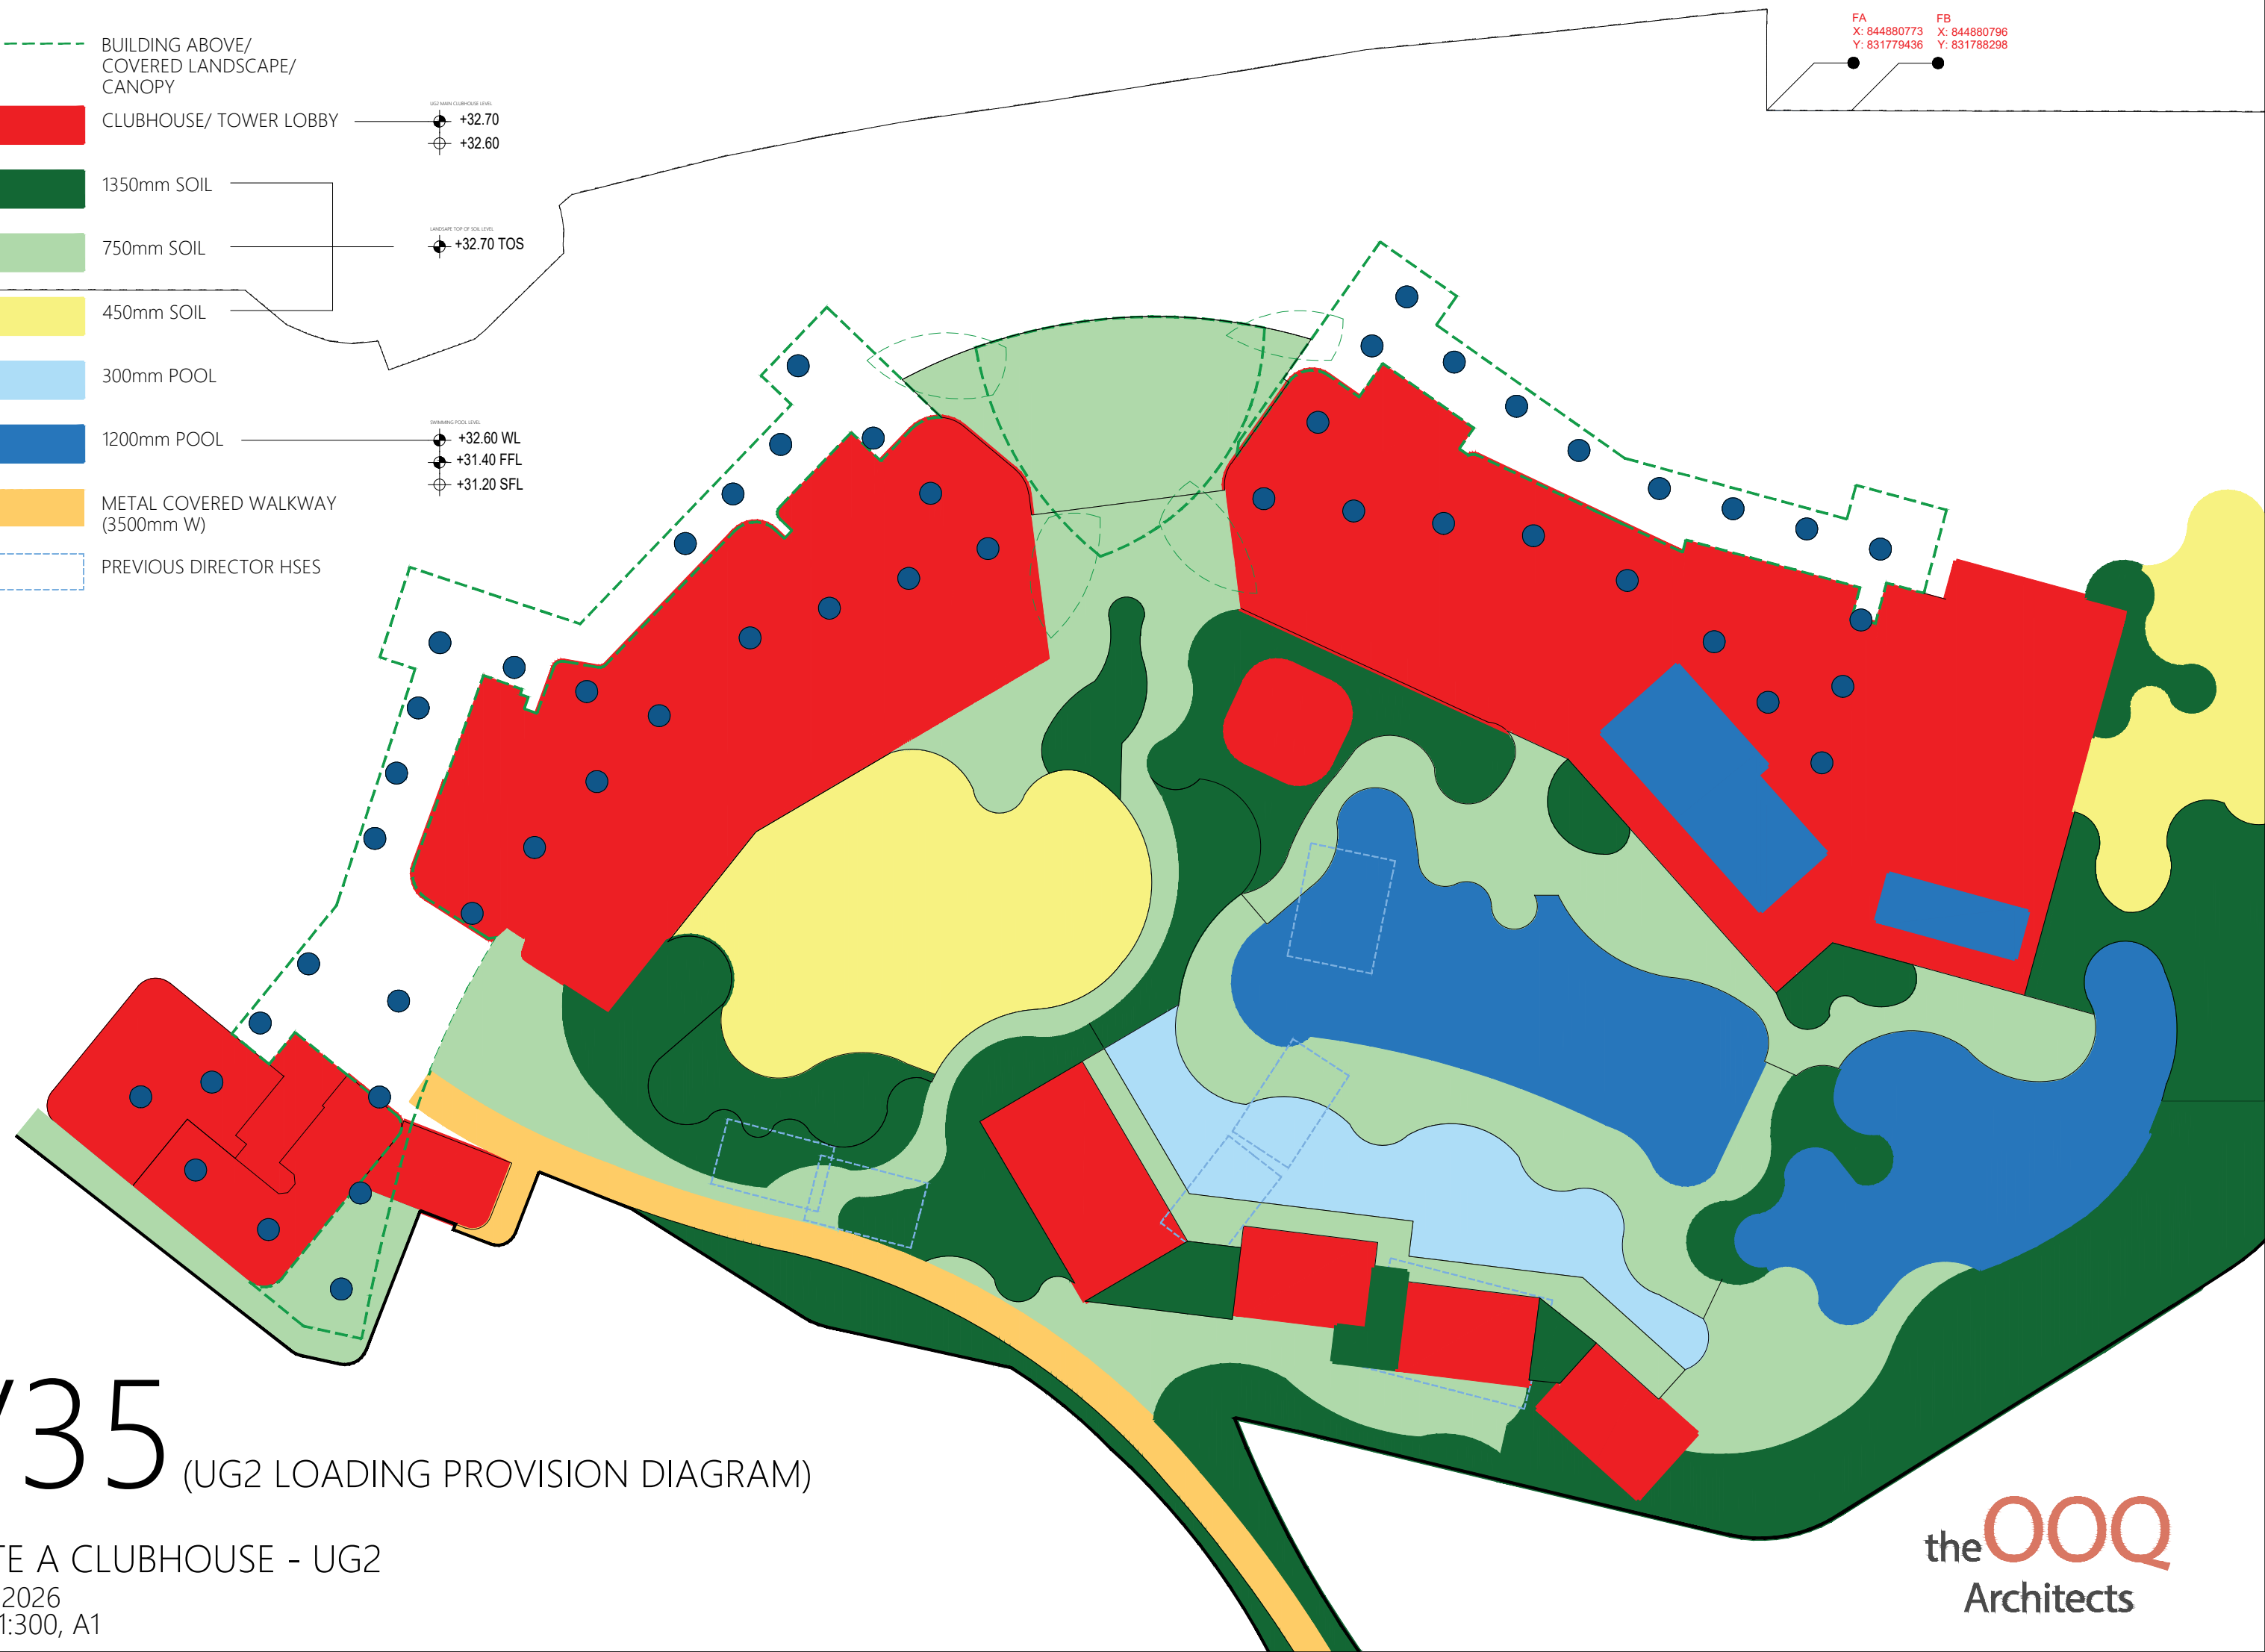

V35 (UG2 LOADING PROVISION DIAGRAM)

SS SITE A CLUBHOUSE - UG2
28 SEP 2026
SCALE 1:300, A1